


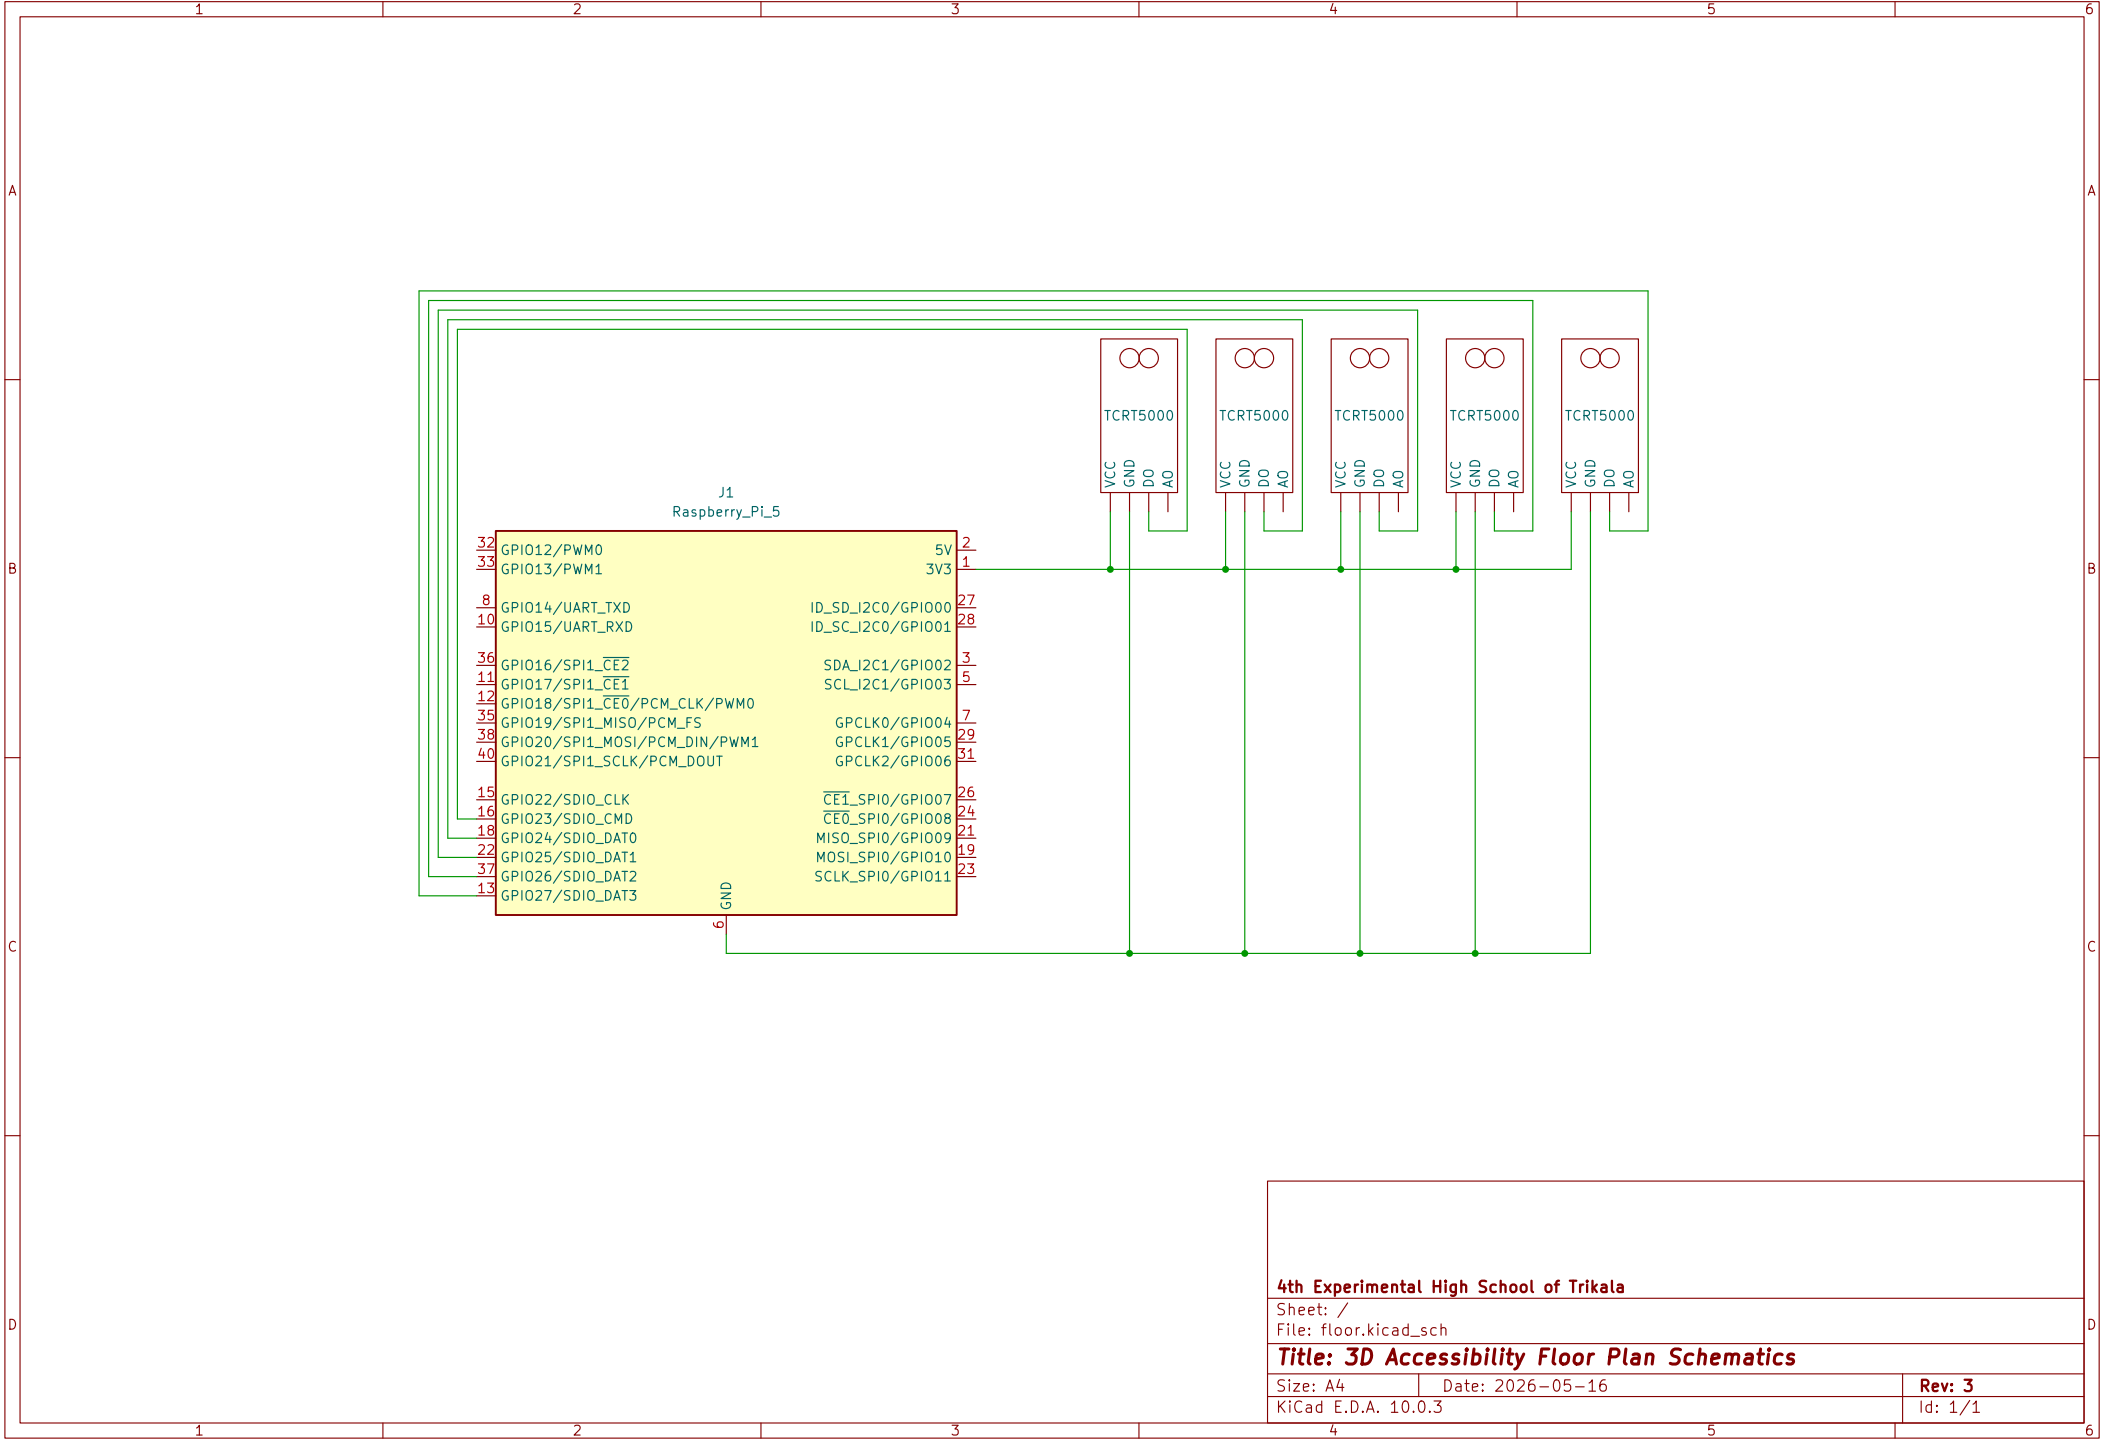

4th Experimental High School of Trikala

Sheet: /
File: floor.kicad_sch

Title: 3D Accessibility Floor Plan Schematics

Size: A4 Date: 2026-05-16

KiCad E.D.A. 10.0.3

Rev: 3

Id: 1/1