


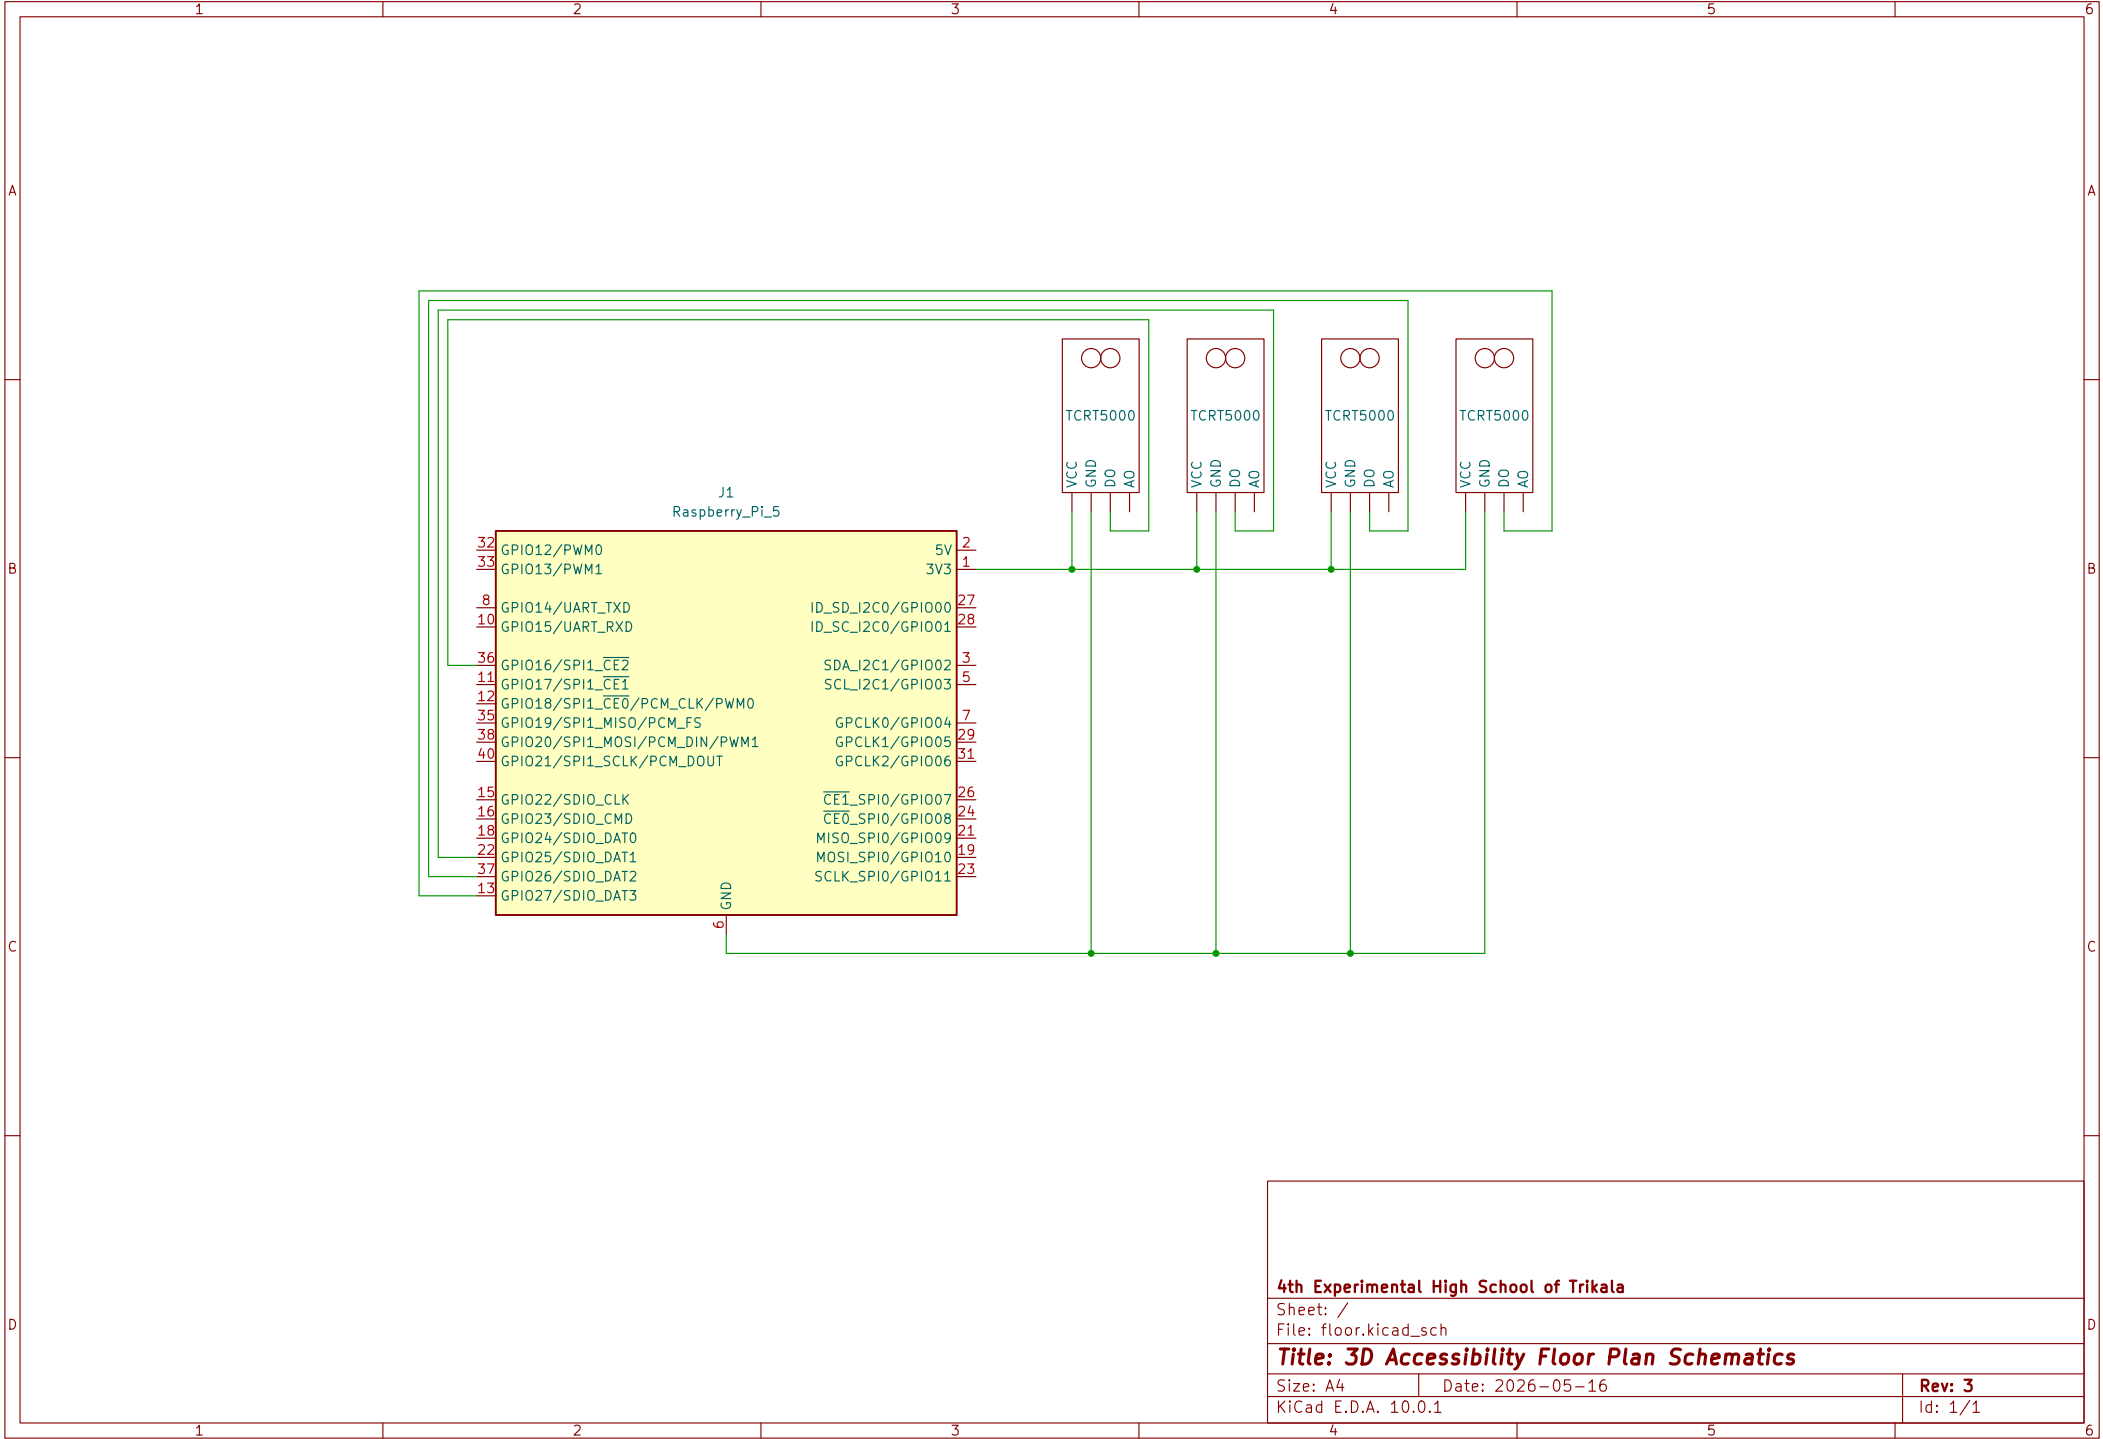

4th Experimental High School of Trikala

Sheet: /
File: floor.kicad_sch

Title: 3D Accessibility Floor Plan Schematics

Size: A4
KiCad E.D.A. 10.0.1

Date: 2026-05-16

Rev: 3
Id: 1/1